DWG. No. REV. FILE No.

| REV. | DATE | PURPOSE | SIGN. |
|---|---|---|---|
| | | | |
| | | | |
| | | | |

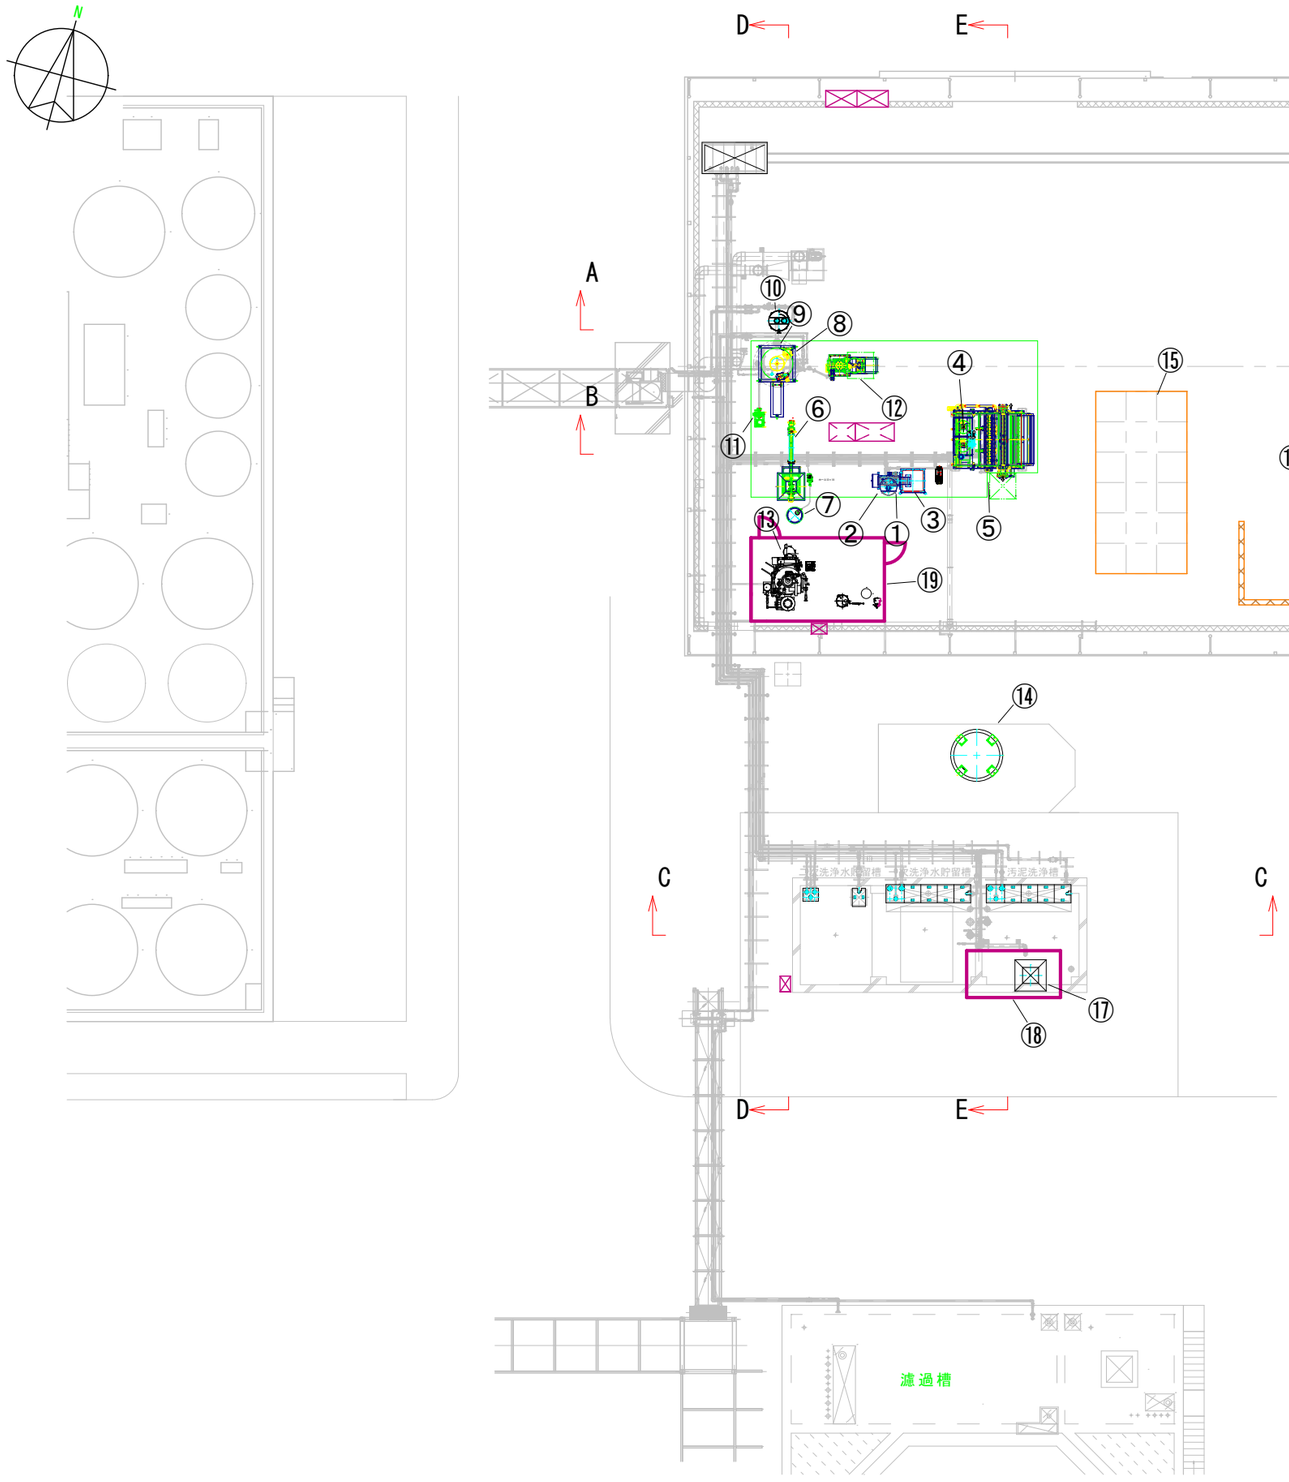


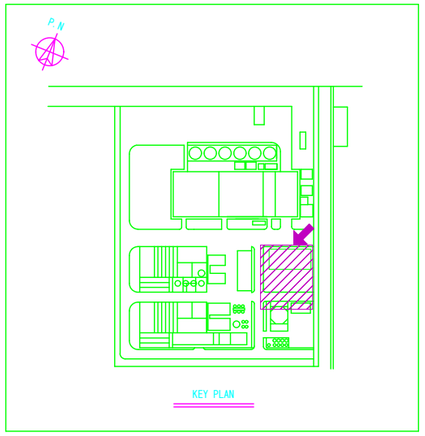


| No. | 名　　称 |
|---|---|
| ⑲ | ボイラー障壁 |
| ⑱ | 汚泥投入口臭気対策ブース |
| ⑰ | 汚泥投入所 |
| ⑯ | 外部汚泥荷下ろし場 |
| ⑮ | 製品コンテナ |
| ⑭ | バルクタンク |
| ⑬ | ボイラー |
| ⑫ | 成型機 |
| ⑪ | 空送装置用ブロワ |
| ⑩ | 復水タンク |
| ⑨ | 復水器 |
| ⑧ | スチームローラー |
| ⑦ | 再生油タンク |
| ⑥ | 混練機 |
| ⑤ | 脱水機 |
| ④ | 凝集槽 |
| ③ | し渣BOX |
| ② | スラリー中継タンク |
| ① | スクリーン |

CONTENTS

| | | | | | | |
|---|---|---|---|---|---|---|
| PLANT 脱水汚泥燃料化施設 | SCALE | DESIGNED BY | DRAWN BY | CHECKED BY | APPROVED BY | DRAWING TITLE 第一期 配置図（平面図） |
| COMPANY 株式会社サニックス資源開発グループ ひびき工場 | 1/200 | '25.07.19 大 平 | '26.01.15 大 平 | | | DWG. No. REV. |

MICRO FILM　FILE No.　A3