DWG. No.	REV.	FILE No.

REV.	DATE	PURPOSE	SIGN.

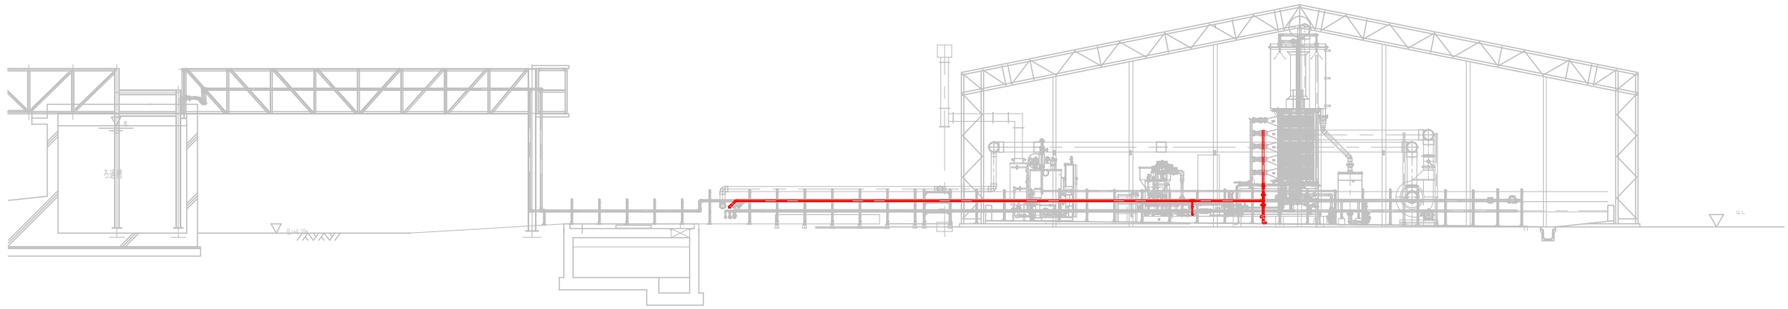

立面図 D-D

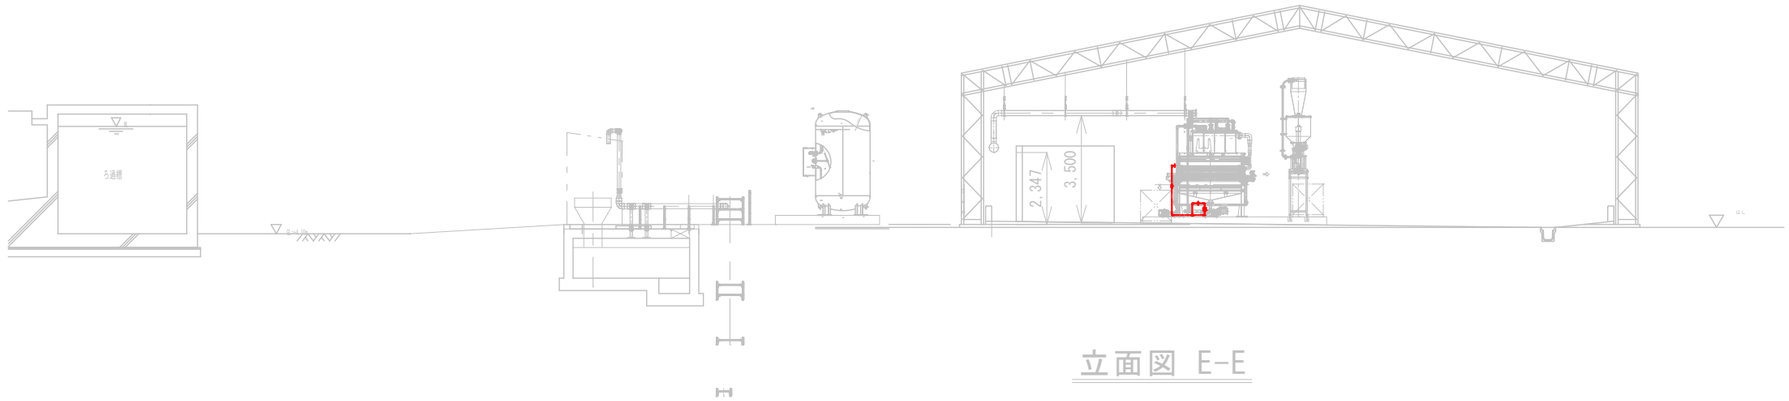

立面図 E-E

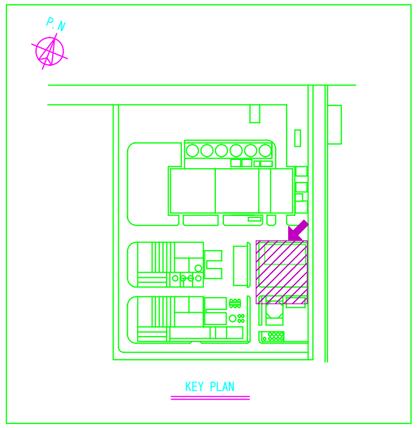

CONTENTS

PLANT	SCALE	DESIGNED BY	DRAWN BY	CHECKED BY	APPROVED BY	DRAWING TITLE
脱水汚泥燃料化施設	1/200	'25.07.19 大平	'26.03.20 大平			配管図4 工水配管（立面図2）
COMPANY 株式会社サニックス資源開発グループ ひびき工場						DWG. No. REV.

MICRO FILM | FILE No. | A3