| DWG. No. | REV. | FILE No. |
|---|---|---|
| | | |

| REV. | DATE | PURPOSE | SIGN. |
|---|---|---|---|
| | | | |
| | | | |
| | | | |

立面図 A-A

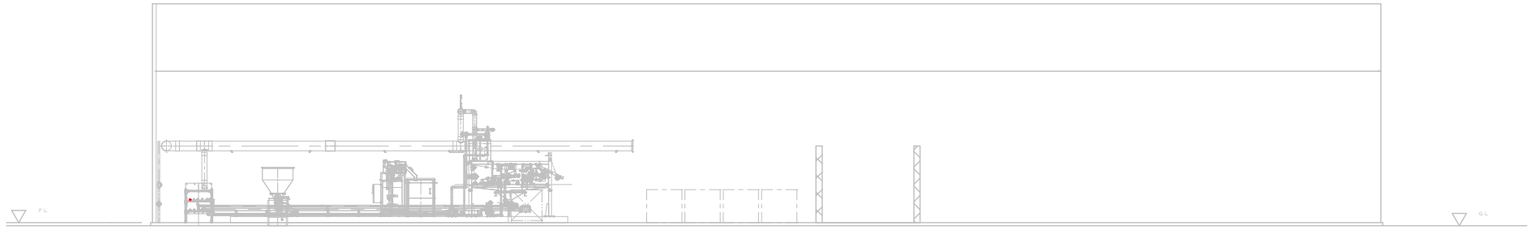

立面図 B-B

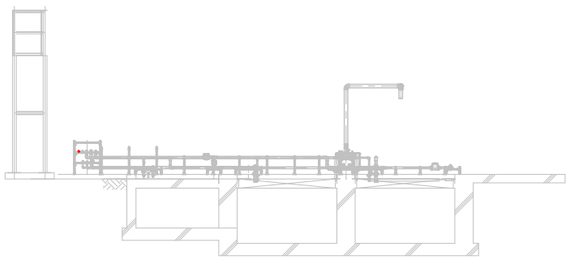

立面図 C-C

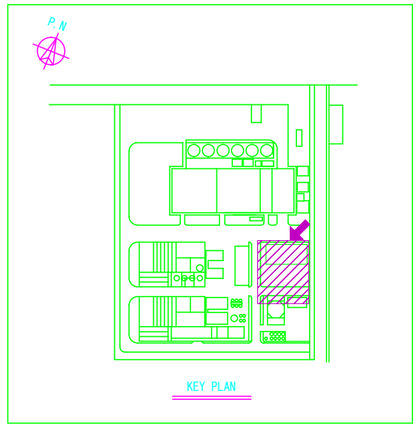


CONTENTS

| PLANT | SCALE | DESIGNED BY | DRAWN BY | CHECKED BY | APPROVED BY | DRAWING TITLE |
|---|---|---|---|---|---|---|
| 脱水汚泥燃料化施設 | 1/200 | '25.07.19 大平 | '26.03.20 大平 | | | 配管図7 冷却水返送配管（立面図1） |
| COMPANY 株式会社サニックス資源開発グループ ひびき工場 | | | | | | DWG. No. REV. |

MICRO FILM | FILE No. | A3