DWG. No.	REV.	FILE No.

REV.	DATE	PURPOSE	SIGN.

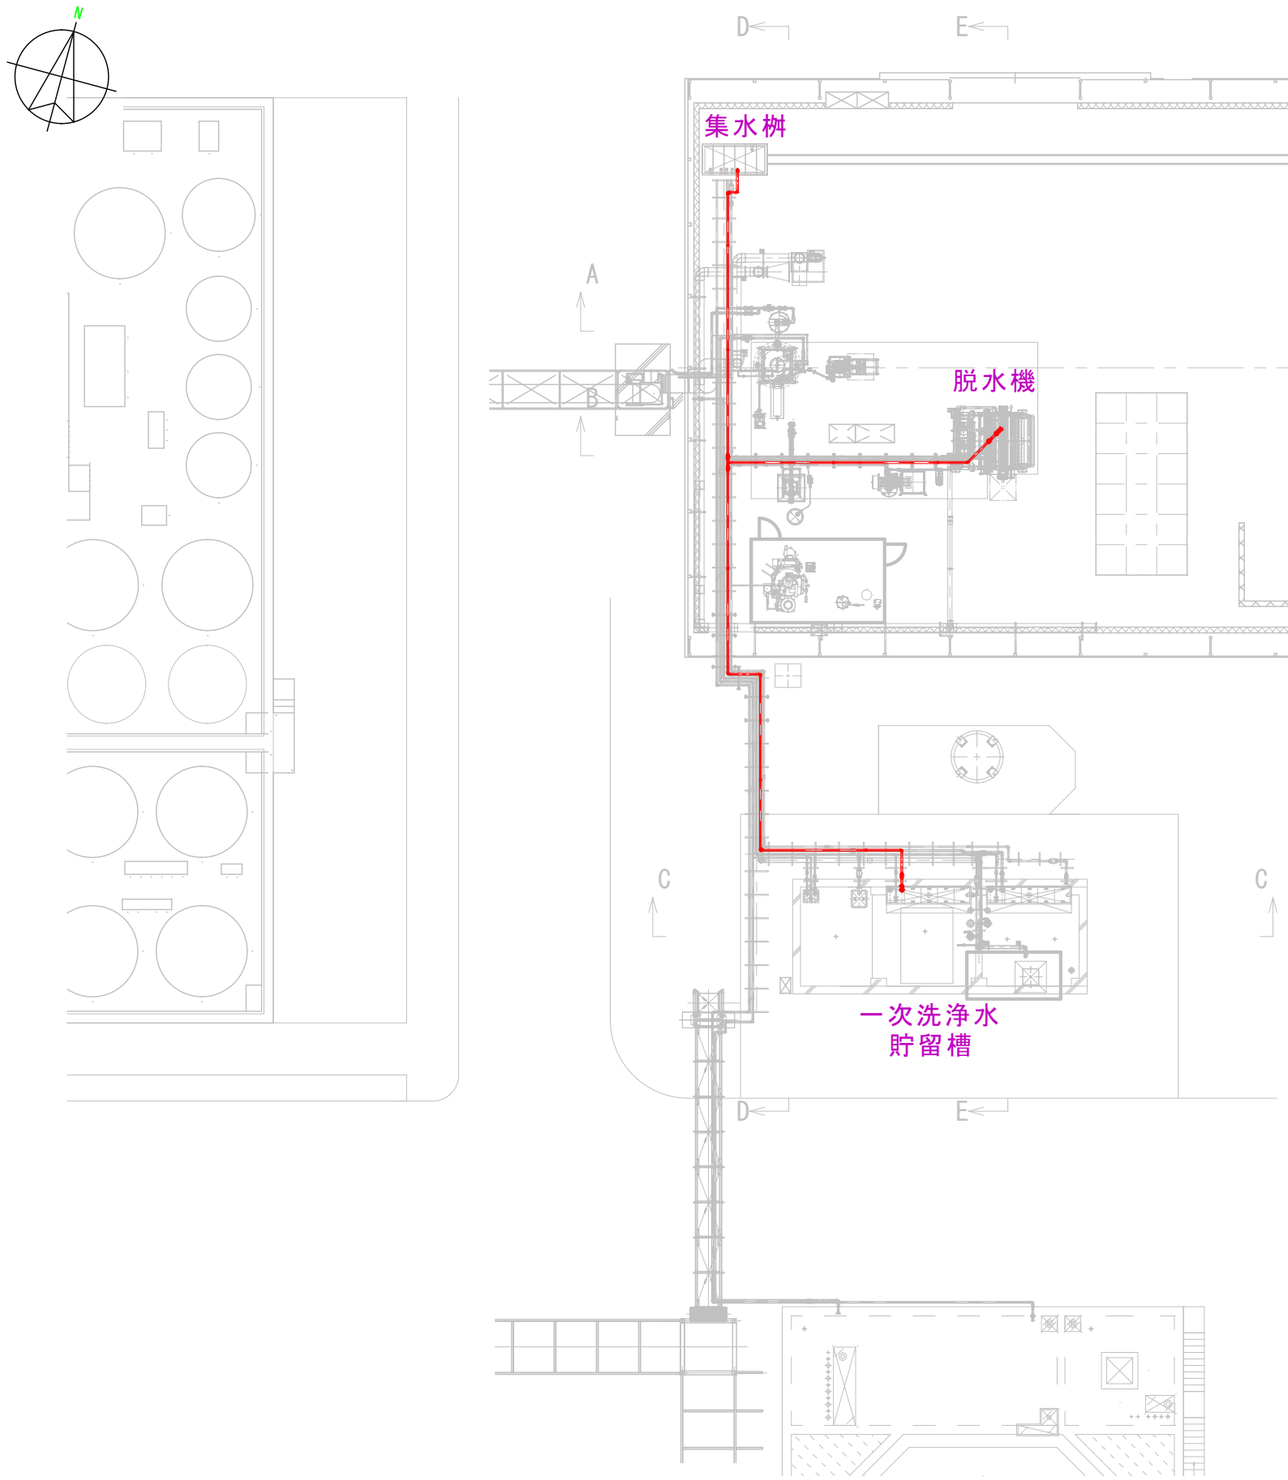

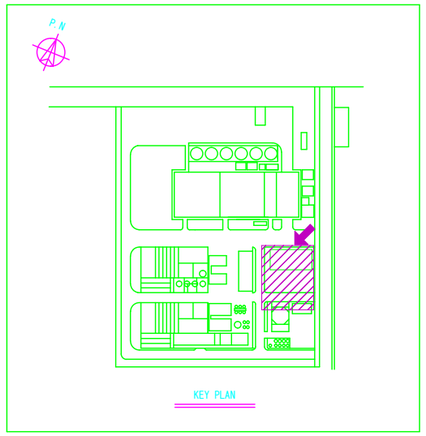

No.	配　管　名　称	移　送　元	移　送　先	管　種、口　径
17	空送配管	空送ブロワ	サイクロン	U-PVC、C-PVC 30A　SGP 32A
16	再生油添加配管	再生油貯留タンク	混練機	ホース 18×12mm　8A
15	集水桝移送配管	集水桝	受ピット	U-PVC VP 100、75、65、50A
14	カチオン添加配管	既設カチオン貯槽	凝集槽A・B	U-PVC VP 25A
13	ボイラースチーム配管	高圧蒸気ボイラー	乾燥機	SGP 32A
12	市水配管	既設市水配管	給水タンク	HI-PVC VP 50、40A
11	スチームドレン配管	乾燥機	二次洗浄水貯留槽	SGP 40、32、25A
10	復水配管	復水器	復水タンク	U-PVC VP 150、100A
9	ろ布洗浄水移送配管	脱水機	二次洗浄水貯留槽	U-PVC VU 40A
8	脱水ろ液移送配管	脱水機	一次洗浄水貯留槽、集水桝	U-PVC VU 65A
7	冷却水返送配管	復水タンク	ろ過槽、混合槽	U-PVC VP 50A
6	冷却水移送配管	ろ過槽	復水器	U-PVC VP 50A
5	スクリーンろ液移送配管	スクリーンろ液タンク	凝集槽A	U-PVC VP 40A
4	工水配管	既設工水配管	汚泥洗浄設備、脱水機	U-PVC VP 50、30、25A
3	洗浄水移送配管	一次・二次洗浄水貯留槽	汚泥洗浄槽、集水桝	U-PVC VP 65A
2	洗浄汚泥移送配管	汚泥洗浄槽	スクリーン	U-PVC VP 50A
1	脱臭配管	汚泥洗浄設備、脱水機	既設φ600脱臭配管	U-PVC、ダクト管 300、150、100、75、50A

CONTENTS

PLANT	SCALE	DESIGNED BY	DRAWN BY	CHECKED BY	APPROVED BY	DRAWING TITLE
脱水汚泥燃料化施設	1/200	'25.07.19 大平	'26.03.20 大平			配管図8　脱水ろ液移送配管（平面図）
COMPANY 株式会社サニックス資源開発グループ　ひびき工場						DWG. No. / REV.

MICRO FILM　FILE No.　A3