DWG. No.	REV.	FILE No.

REV.	DATE	PURPOSE	SIGN.

立面図 A-A

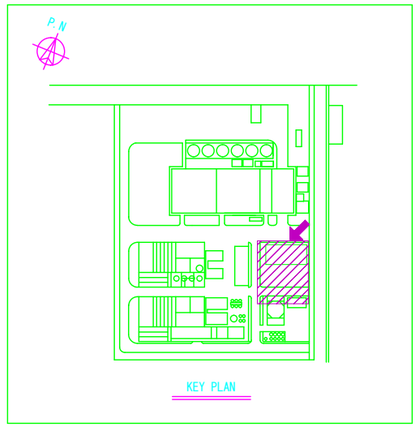

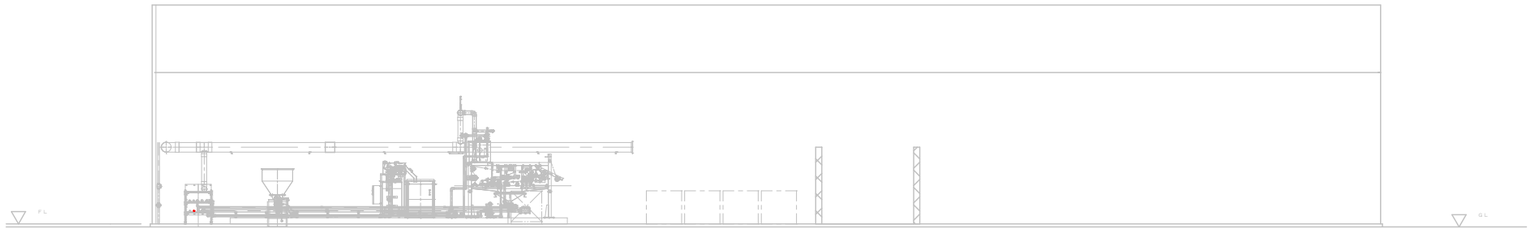

立面図 B-B

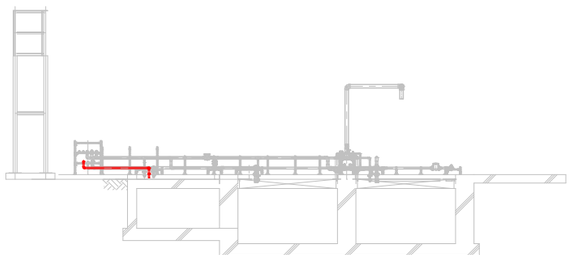

立面図 C-C

CONTENTS

PLANT	脱水汚泥燃料化施設
COMPANY	株式会社サニックス資源開発グループ ひびき工場

SCALE	DESIGNED BY	DRAWN BY	CHECKED BY	APPROVED BY
1/200	'25.07.19 大 平	'26.03.20 大 平		

DRAWING TITLE: 配管図11 スチームドレン配管（立面図1）

DWG. No. REV.

MICRO FILM | FILE No. | A3