DWG. No.	REV.	FILE No.

REV.	DATE	PURPOSE	SIGN.

立面図 A-A

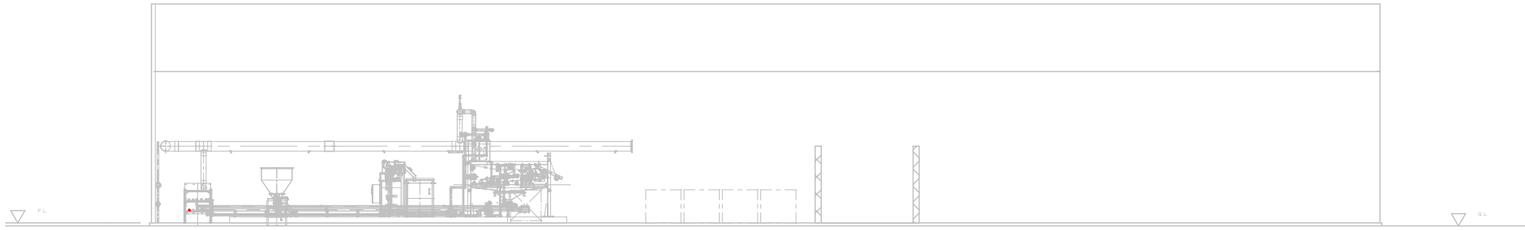

立面図 B-B

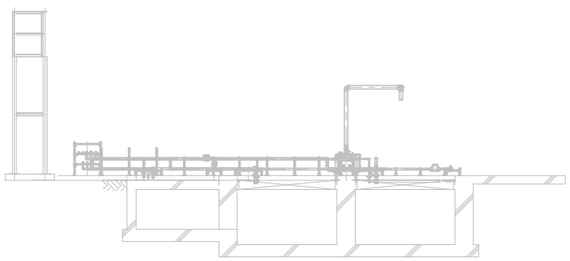

立面図 C-C

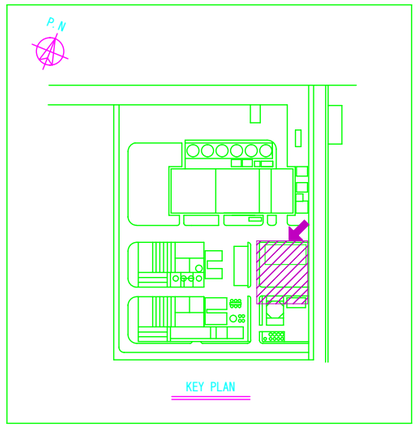

CONTENTS

PLANT	SCALE	DESIGNED BY	DRAWN BY	CHECKED BY	APPROVED BY	DRAWING TITLE
脱水汚泥燃料化施設	1/200	'25.07.19 大平	'26.03.20 大平			配管図12 市水配管（立面図1）
COMPANY 株式会社サニックス資源開発グループ ひびき工場						DWG. No. REV.

MICRO FILM | FILE No. | A3