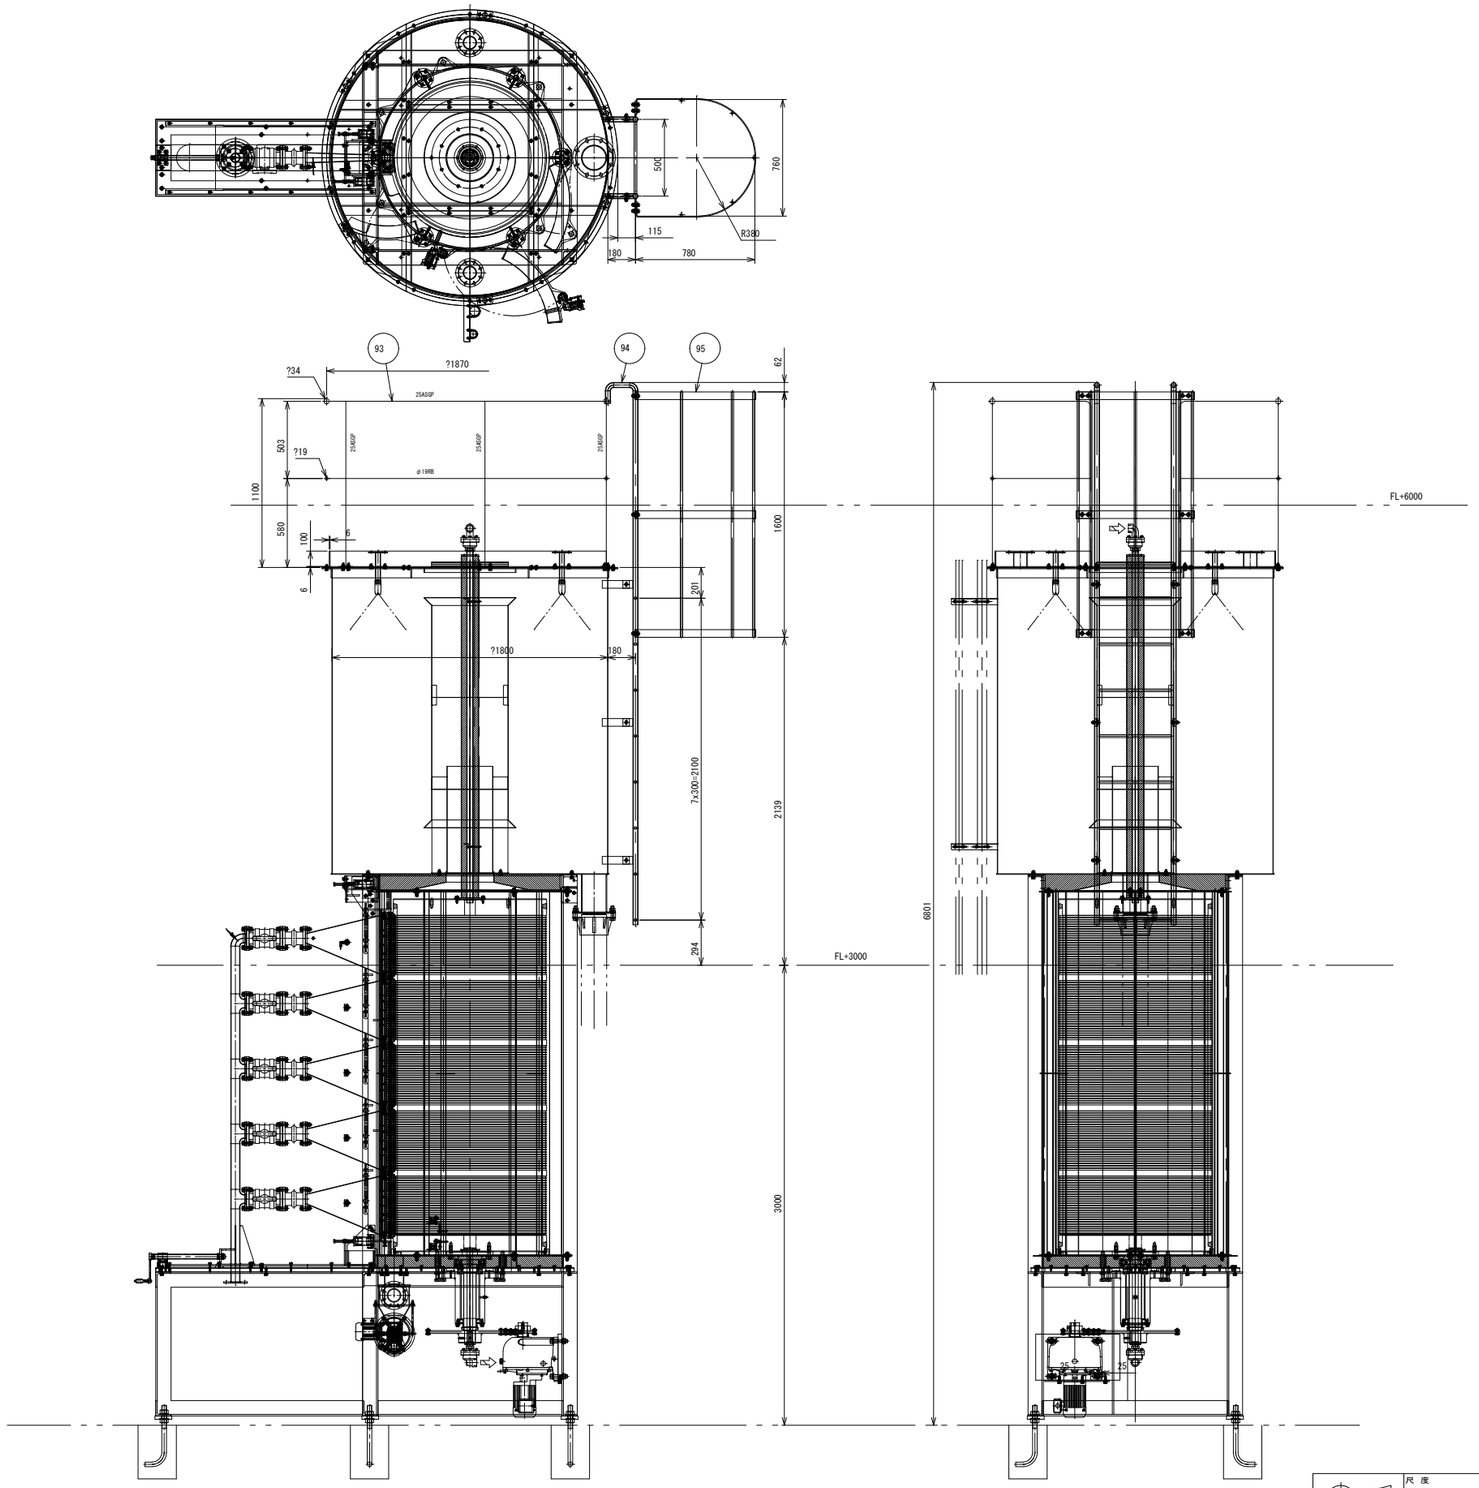


| 記号 | 日付 | 改訂内容 | 作成者 |
|---|---|---|---|
| 1 | | | |
| 2 | | | |
| 3 | | | |

| | | | |
|---|---|---|---|
| 尺度 1：20 | サイズ A1 | 機器 有機性汚泥燃料施設 | 部品名 乾燥機・復水器 組立図 |
| 株式会社 アクアトリム | 製図 寺田 | 型式 | 図面番号 AT-221121-07-5 |
| | | 作成日 2025.06.23 | 個数 |