番号	日付	作図	担当	改定記事
0	'25.04.05	藤田	菊池	新規作成
1	'25.12.27	藤田	菊池	機器配置変更
2	'26.01.14	平山	菊池	寸法等修正
3	'26.01.23	平山	菊池	間仕切り追加

品番	品名	型式	個数
1	貫流蒸気ボイラ	AI-500 20S	1
2	全自動軟水装置	MS-22F	2
3	給水タンク	100L 02	1
4	薬注装置	CPI-10L	1

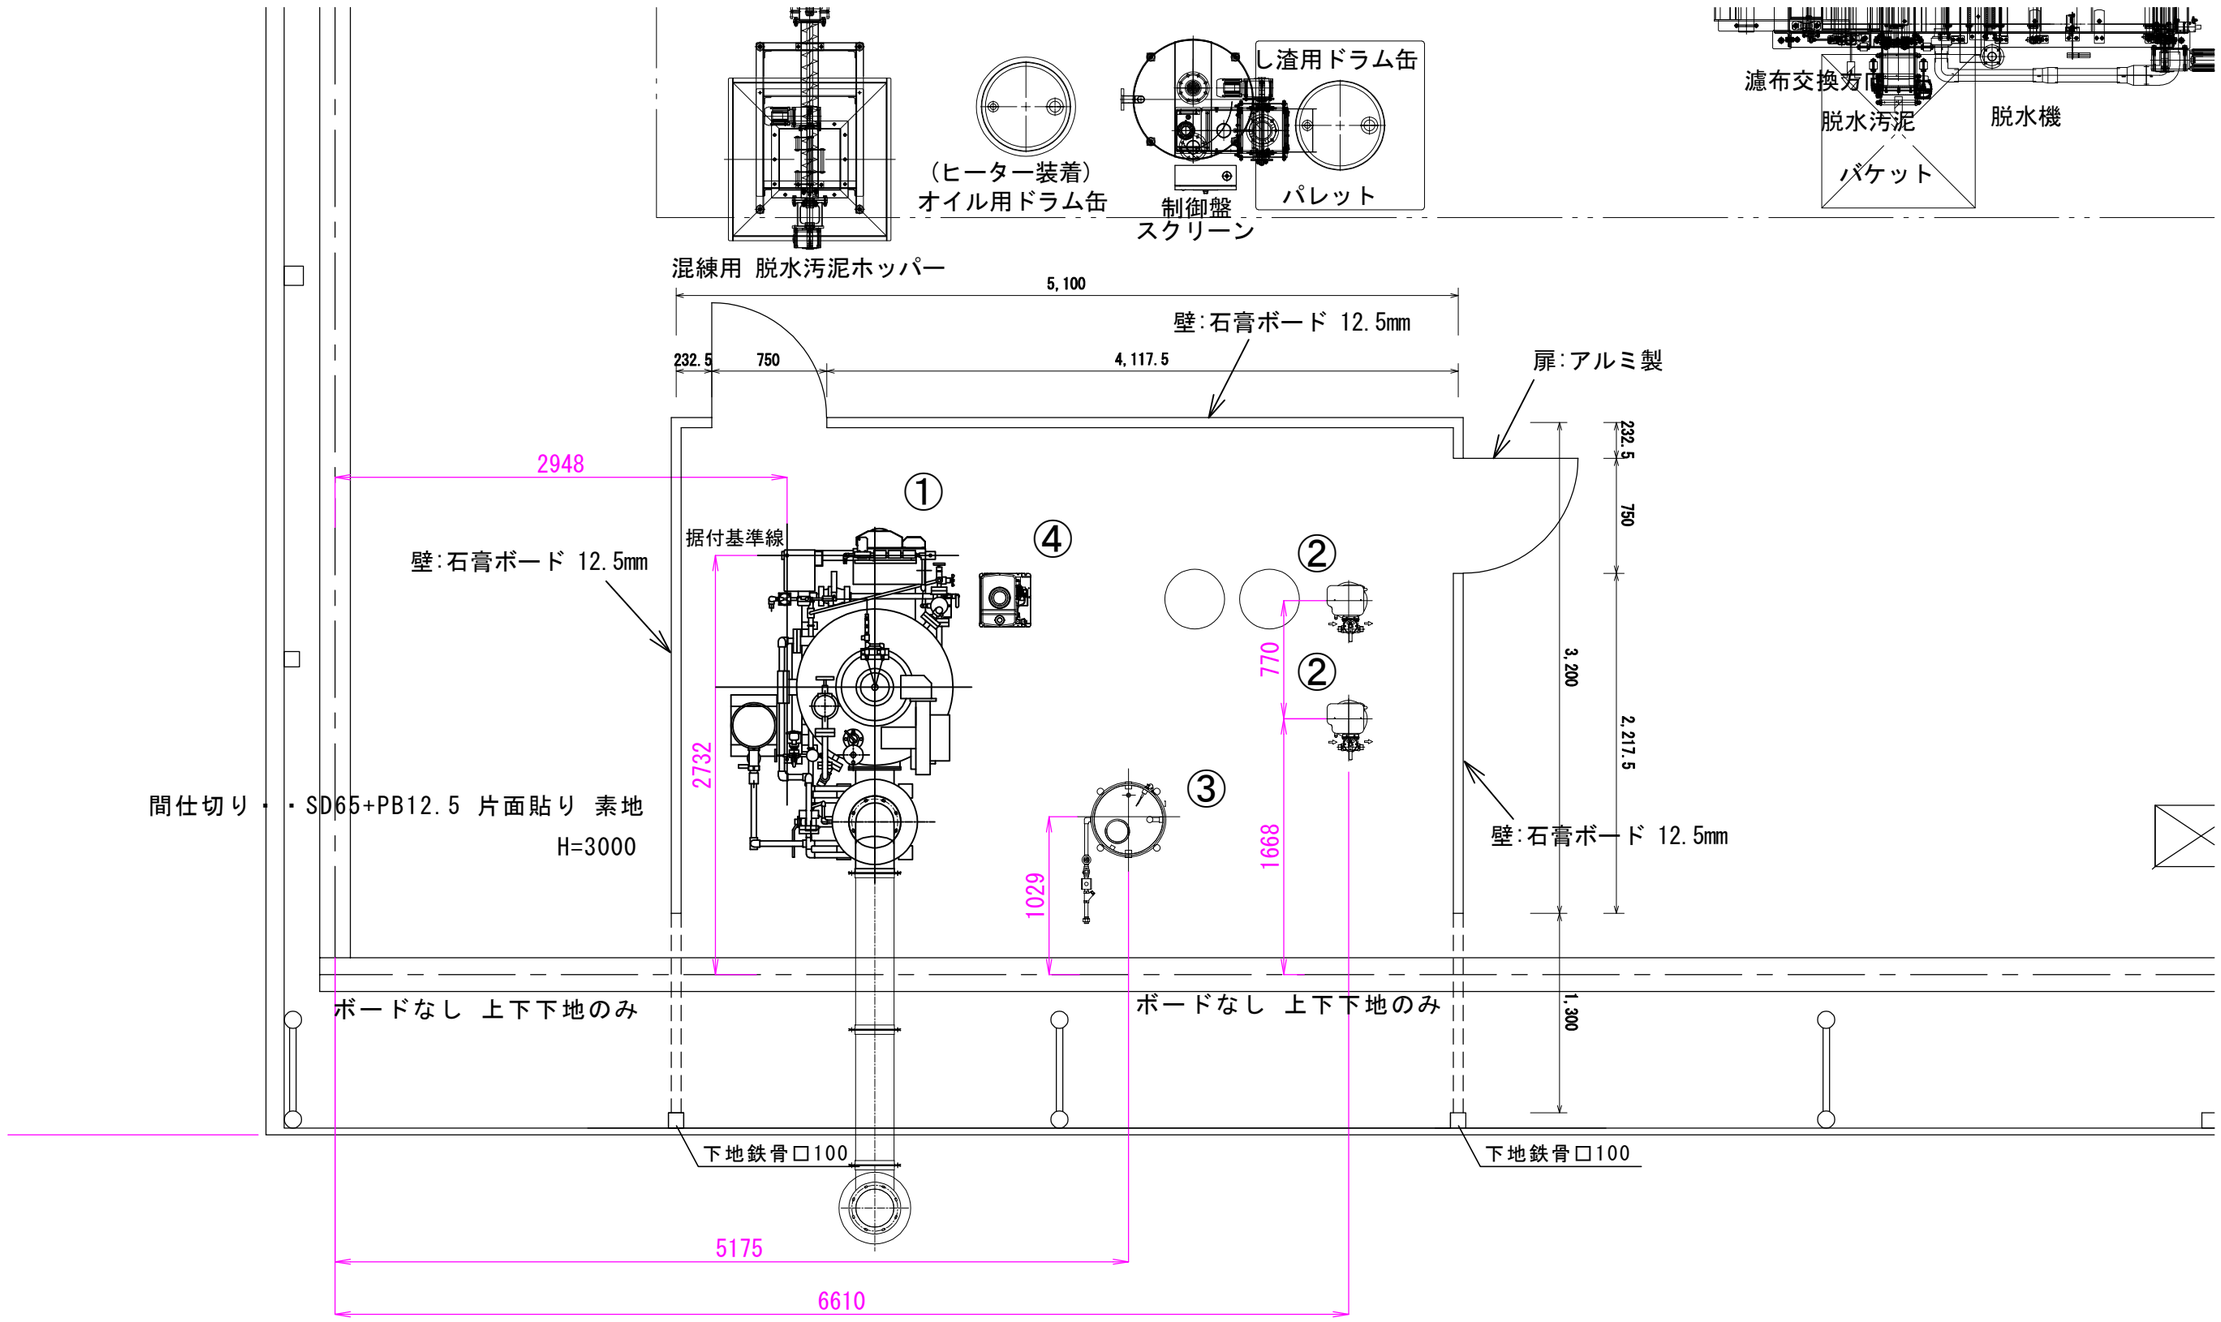

	承認	検図	作図	納入先	株式会社サニックス資源開発グループ ひびき工場 様
MIURA	'26.01.28 菊池	'26.01.28 菊池	'26.01.28 平山	図名	機器配置図
三浦工業株式会社	縮尺 1:40	用紙 A3		図番	28075-24074-03-3